

Niniejszy rysunek jest chroniony prawem autorskim dłuższy niż przez 2 lata od daty wykonania.
Do tym okresie wymaga zezwolenia.


10 ▽ V

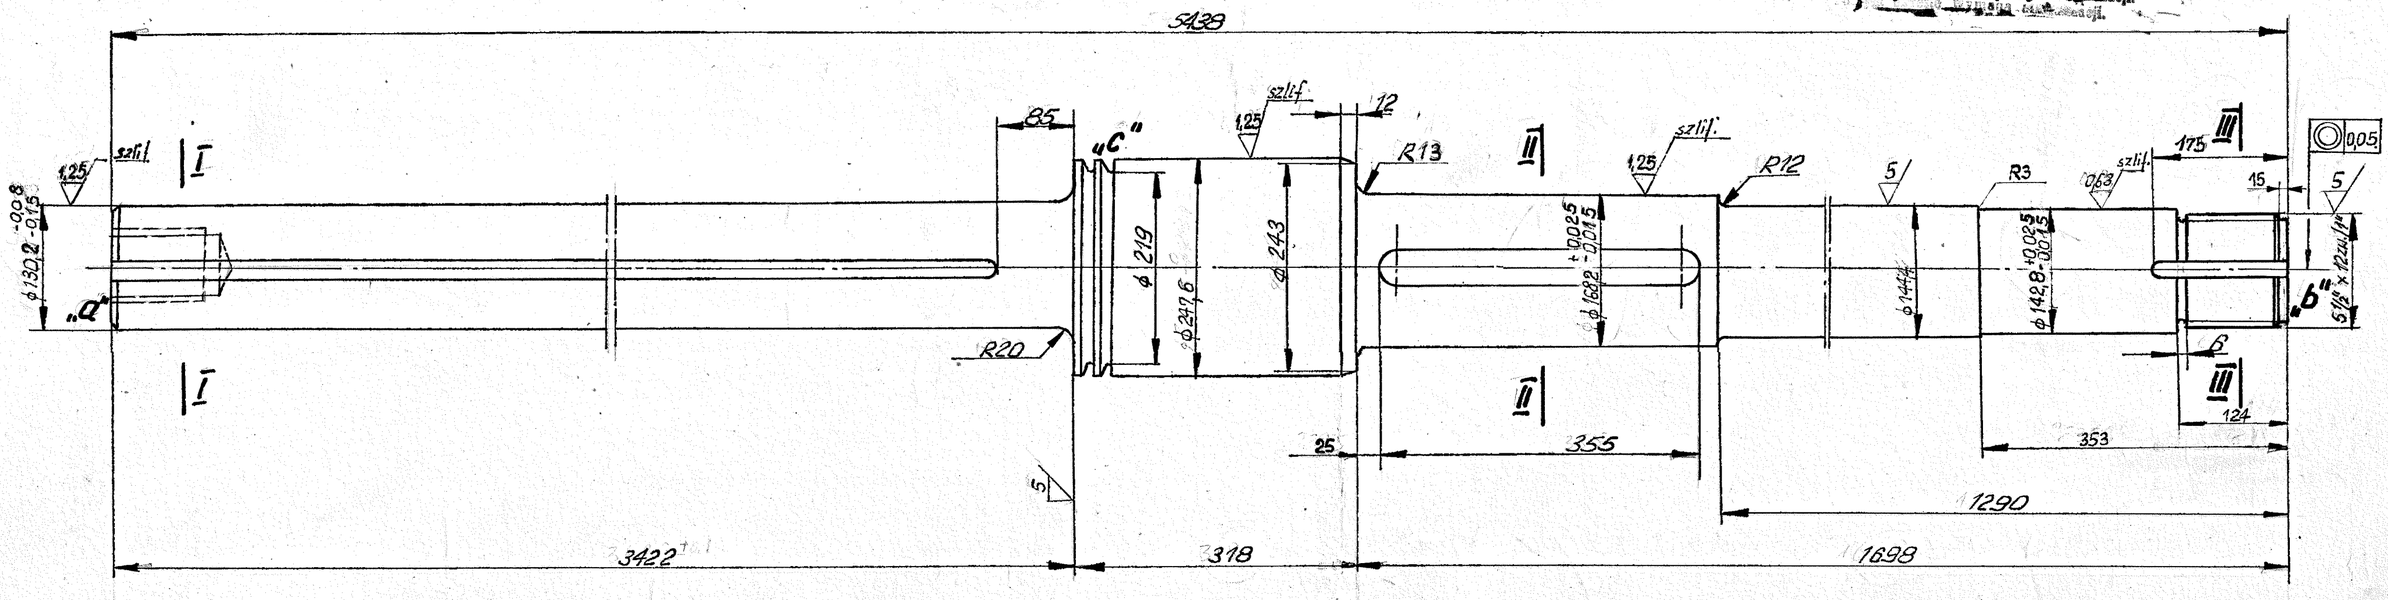


I - I
1:2,5

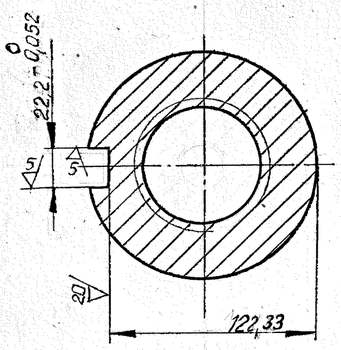


II - II
1:2,5

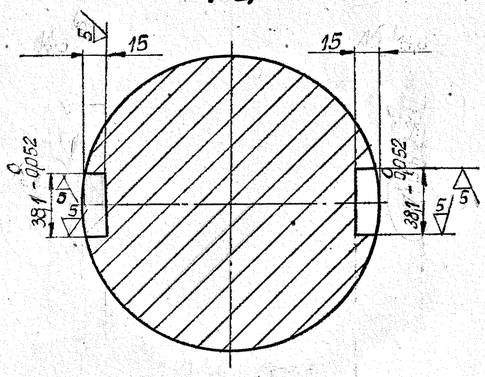


III - III
1:2,5

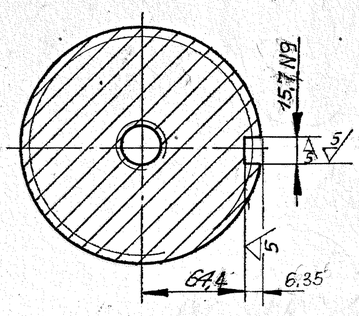


"a"
1:2,5

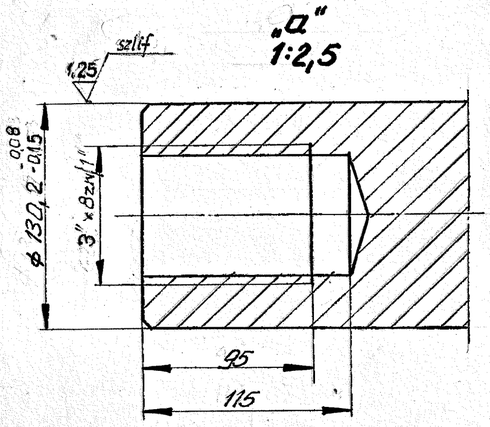

b
1:2,5

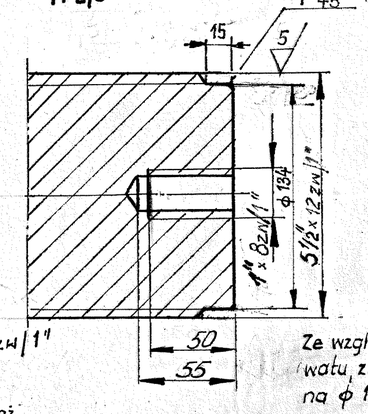

"c"
1:1

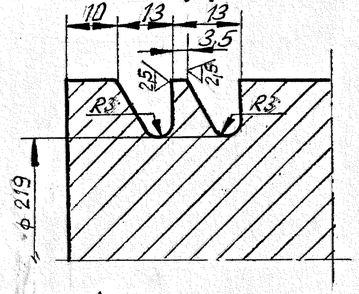

Uwaga:

1. Rysunek wykonano na podstawie istniejącego wału.
2. W miejscu widocznym należy wybić Nr seryjny 22234.

22807

Zmiana ③
Zmieniono końcówkę wału z gwintem 5½" x 12 zw/1" na długości 15mm średnica ϕ 134
07.96r. mgr inż. M. Szpak

Zmiana ②
Ze względu na wykananie wału, zmieniono tolerancje na ϕ 130,2; 168,2; 142,8 oraz obróbkę stanu pow.
M. Madrzejewski

Zmiana ①
Uaktualniono wymiary częściami współpracującymi
dnia 17. XI. 80
M. Madrzejewski

		Wał ϕ 248 l = 5438	1H18N10MT		683	
Ilość szt.	Lp.	Wyszczególnienie	Materiał	Jedn. Masa	Całk. Masa	Nr normy lub rys.

ZAKŁADY CHEMICZNE ZACHO OŚWIĘCIM
ZAKŁAD PROJEKTOWY
PTR

C2.70938.07

Podziałka 1:5 1:2,5; 1:1

Ekspander - Ślimak rys. C2-70938.00

Wał Lp. 5

F-139

	Data	Nazwisko	Podpis	Zastępuje
Projektant	Listopad 1976r.			Zastąpiono
Konstruktor		M. Madrzejewski		
Kreślarz		E. Biatas		Zmiana:
Kier. zesp.		Inż. K. Stasiewski		
Weryfikator		Inż. F. Bilski		
Kier. prac.		Inż. Cz. Urbaniec		

c b a
Wykon.

① ② ③